

**TOPOGRAPHICAL SURVEY ON PLOT NO. 36 GEDE KIREPWE B /36
KILIFI COUNTY**

CLIENT
Kiruti & Co. Adv
Concert House ,Wood Gardens
Wood Avenue ,Kilimani
Nairobi

- LEGEND**
- BOUNDARY AS PER GROUND
 - BOUNDARYWALL
 - ACCESS ROAD
 - POWERLINE
 - CONTOURS
 - BENCH MARK
 - SPOT HEIGHTS
 - PALM TREE
 - TREES


NOTES

DATUM:GEDE DABASO REGISTRATION
SECTION SHEET NO.16


GROUND AREA=0.420Ha(1.04acres)


SCALE 1:1000

25TH APRIL 2025

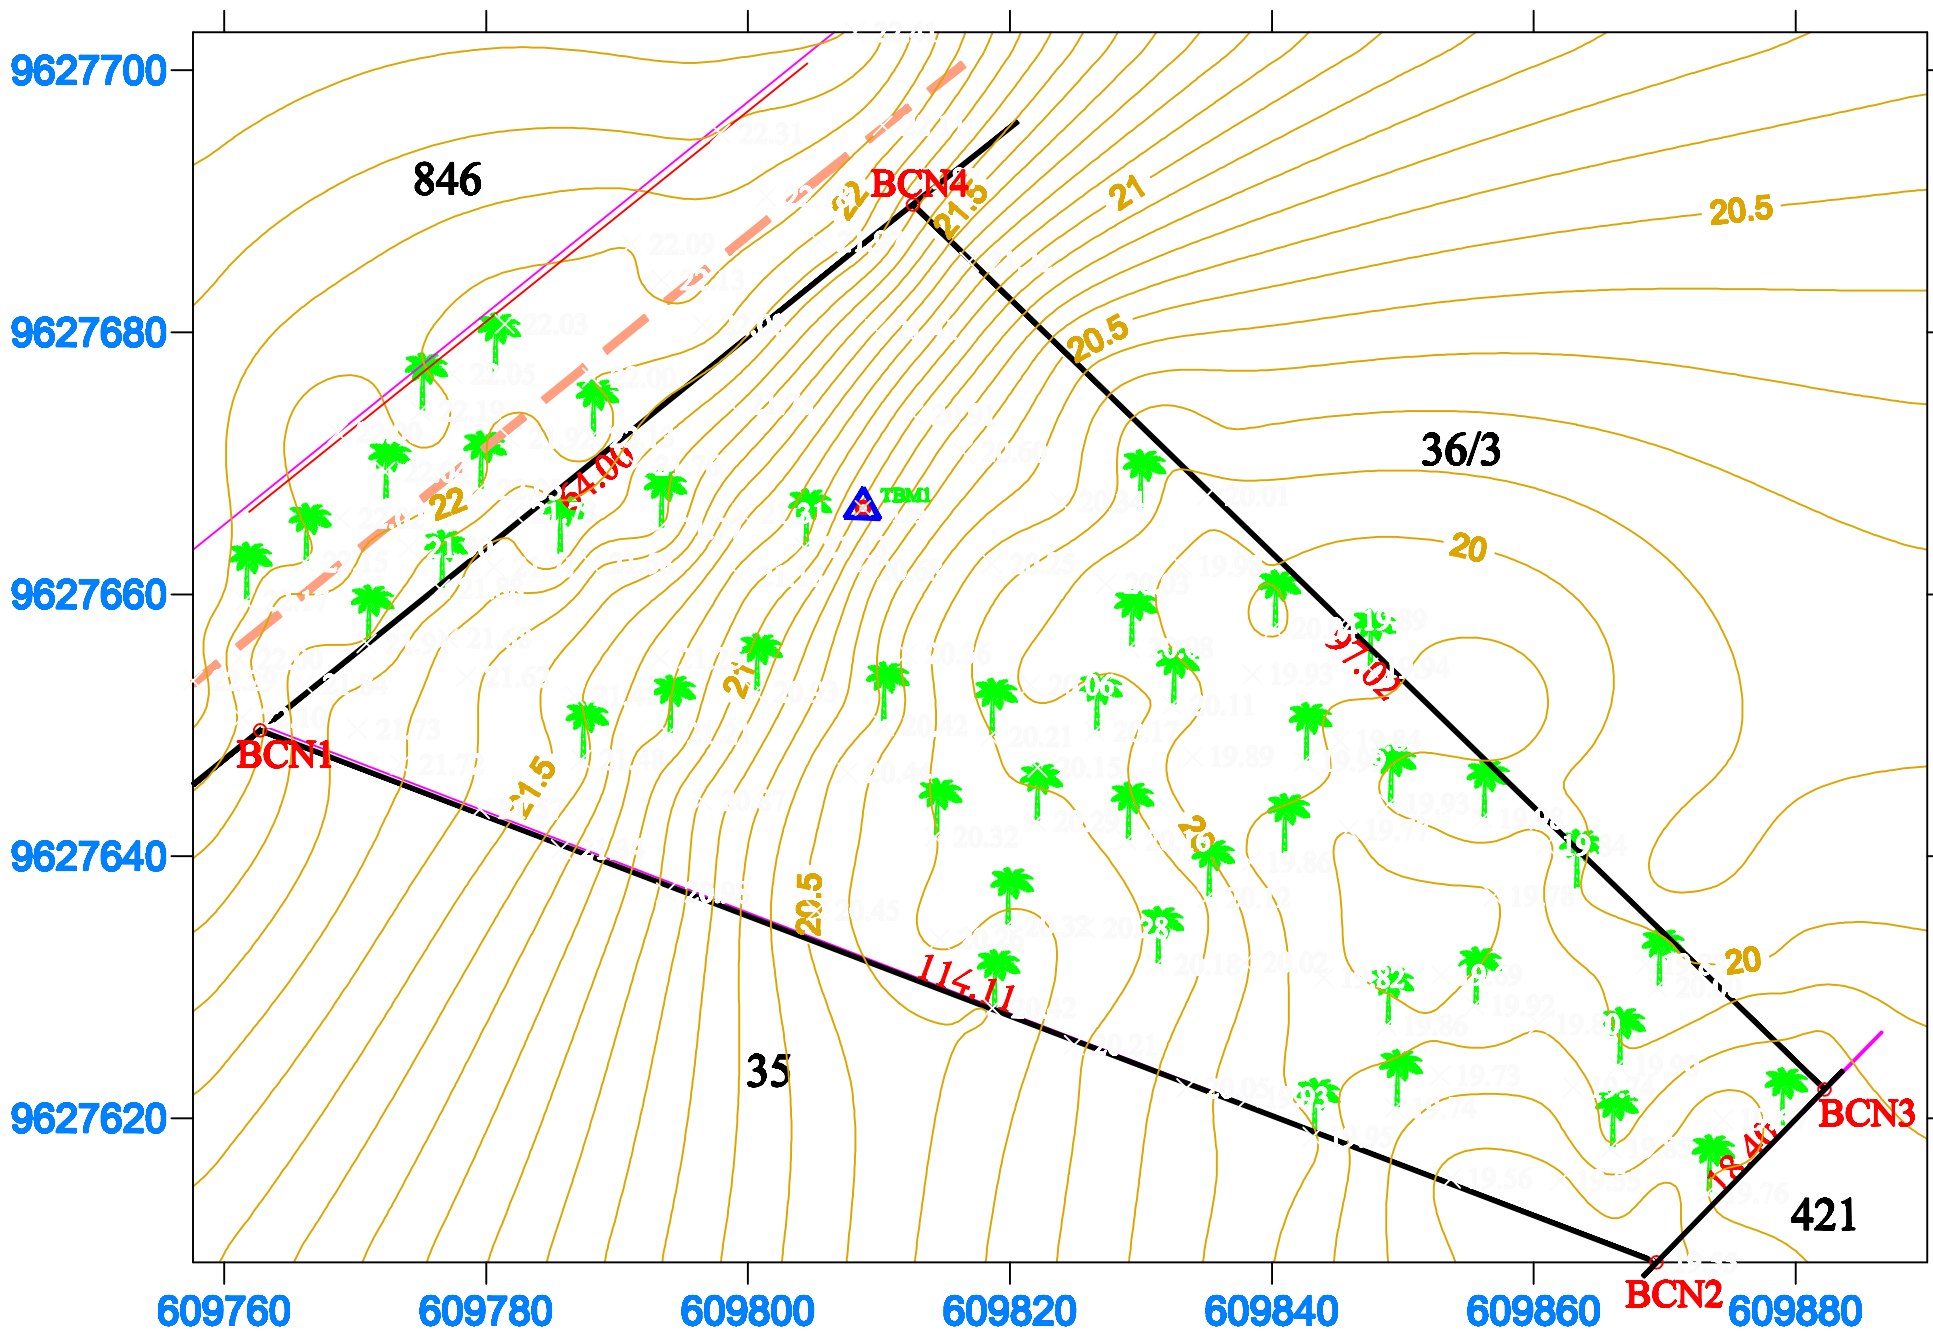


SITE PLAN

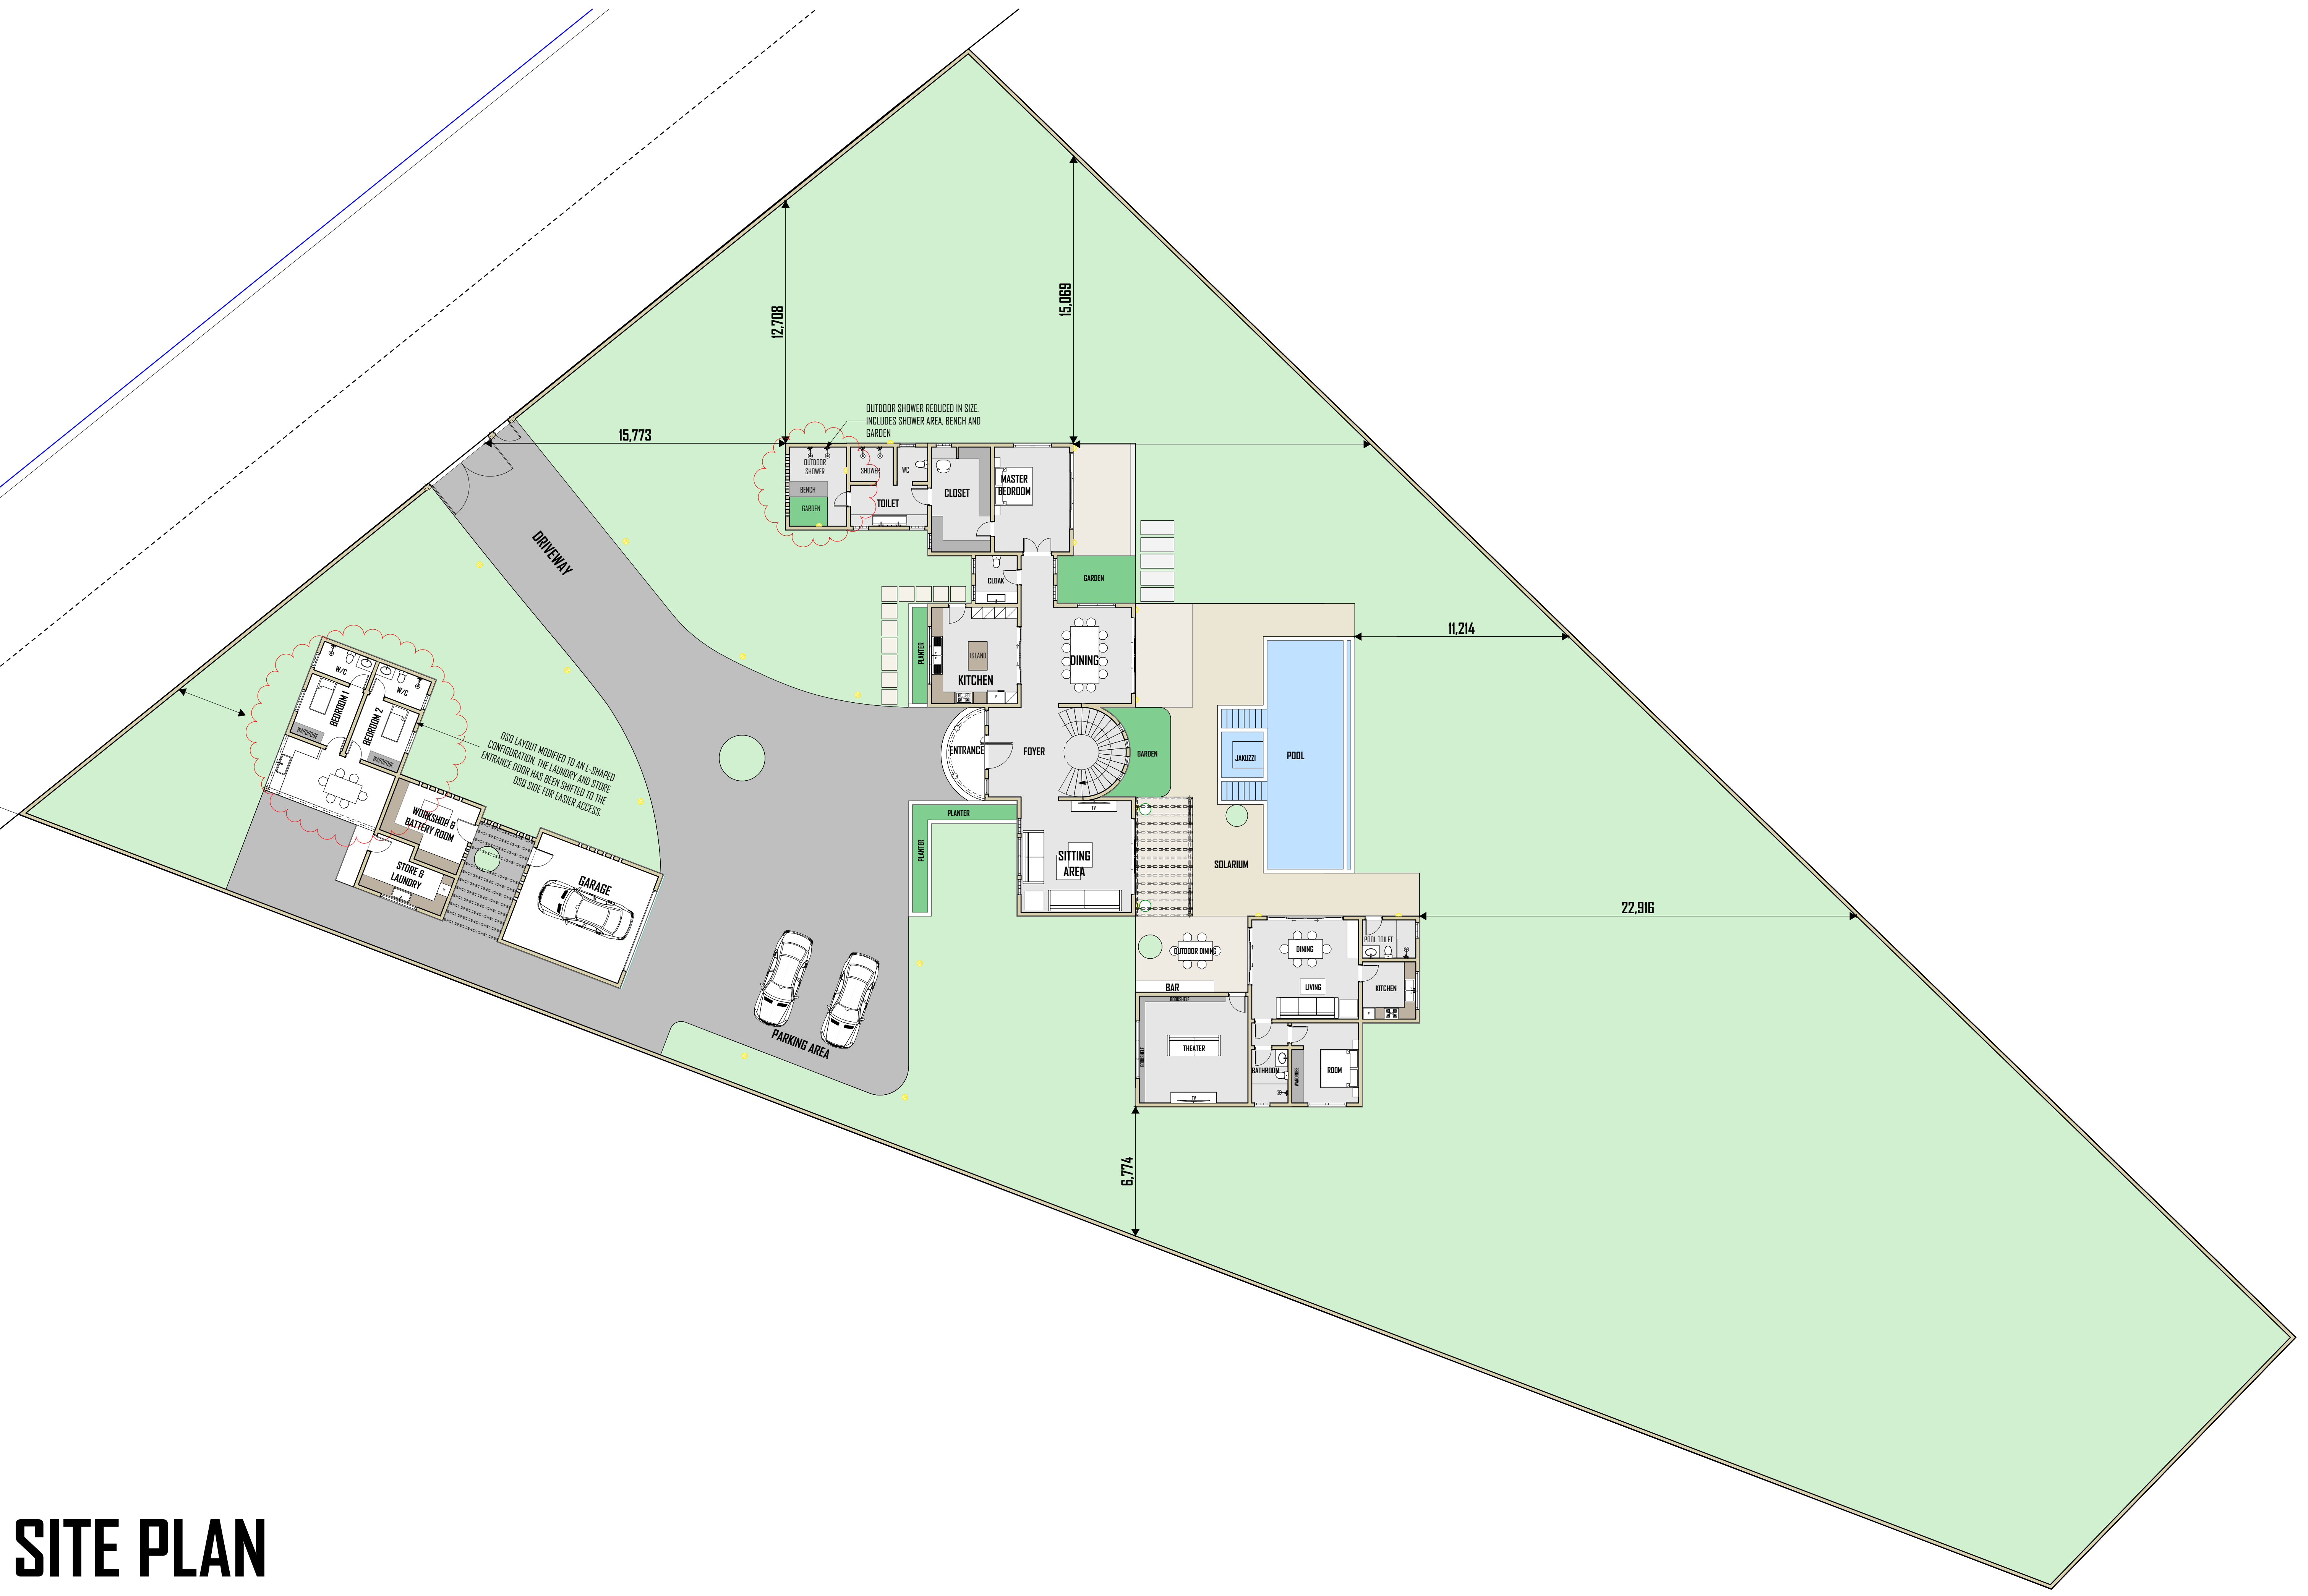


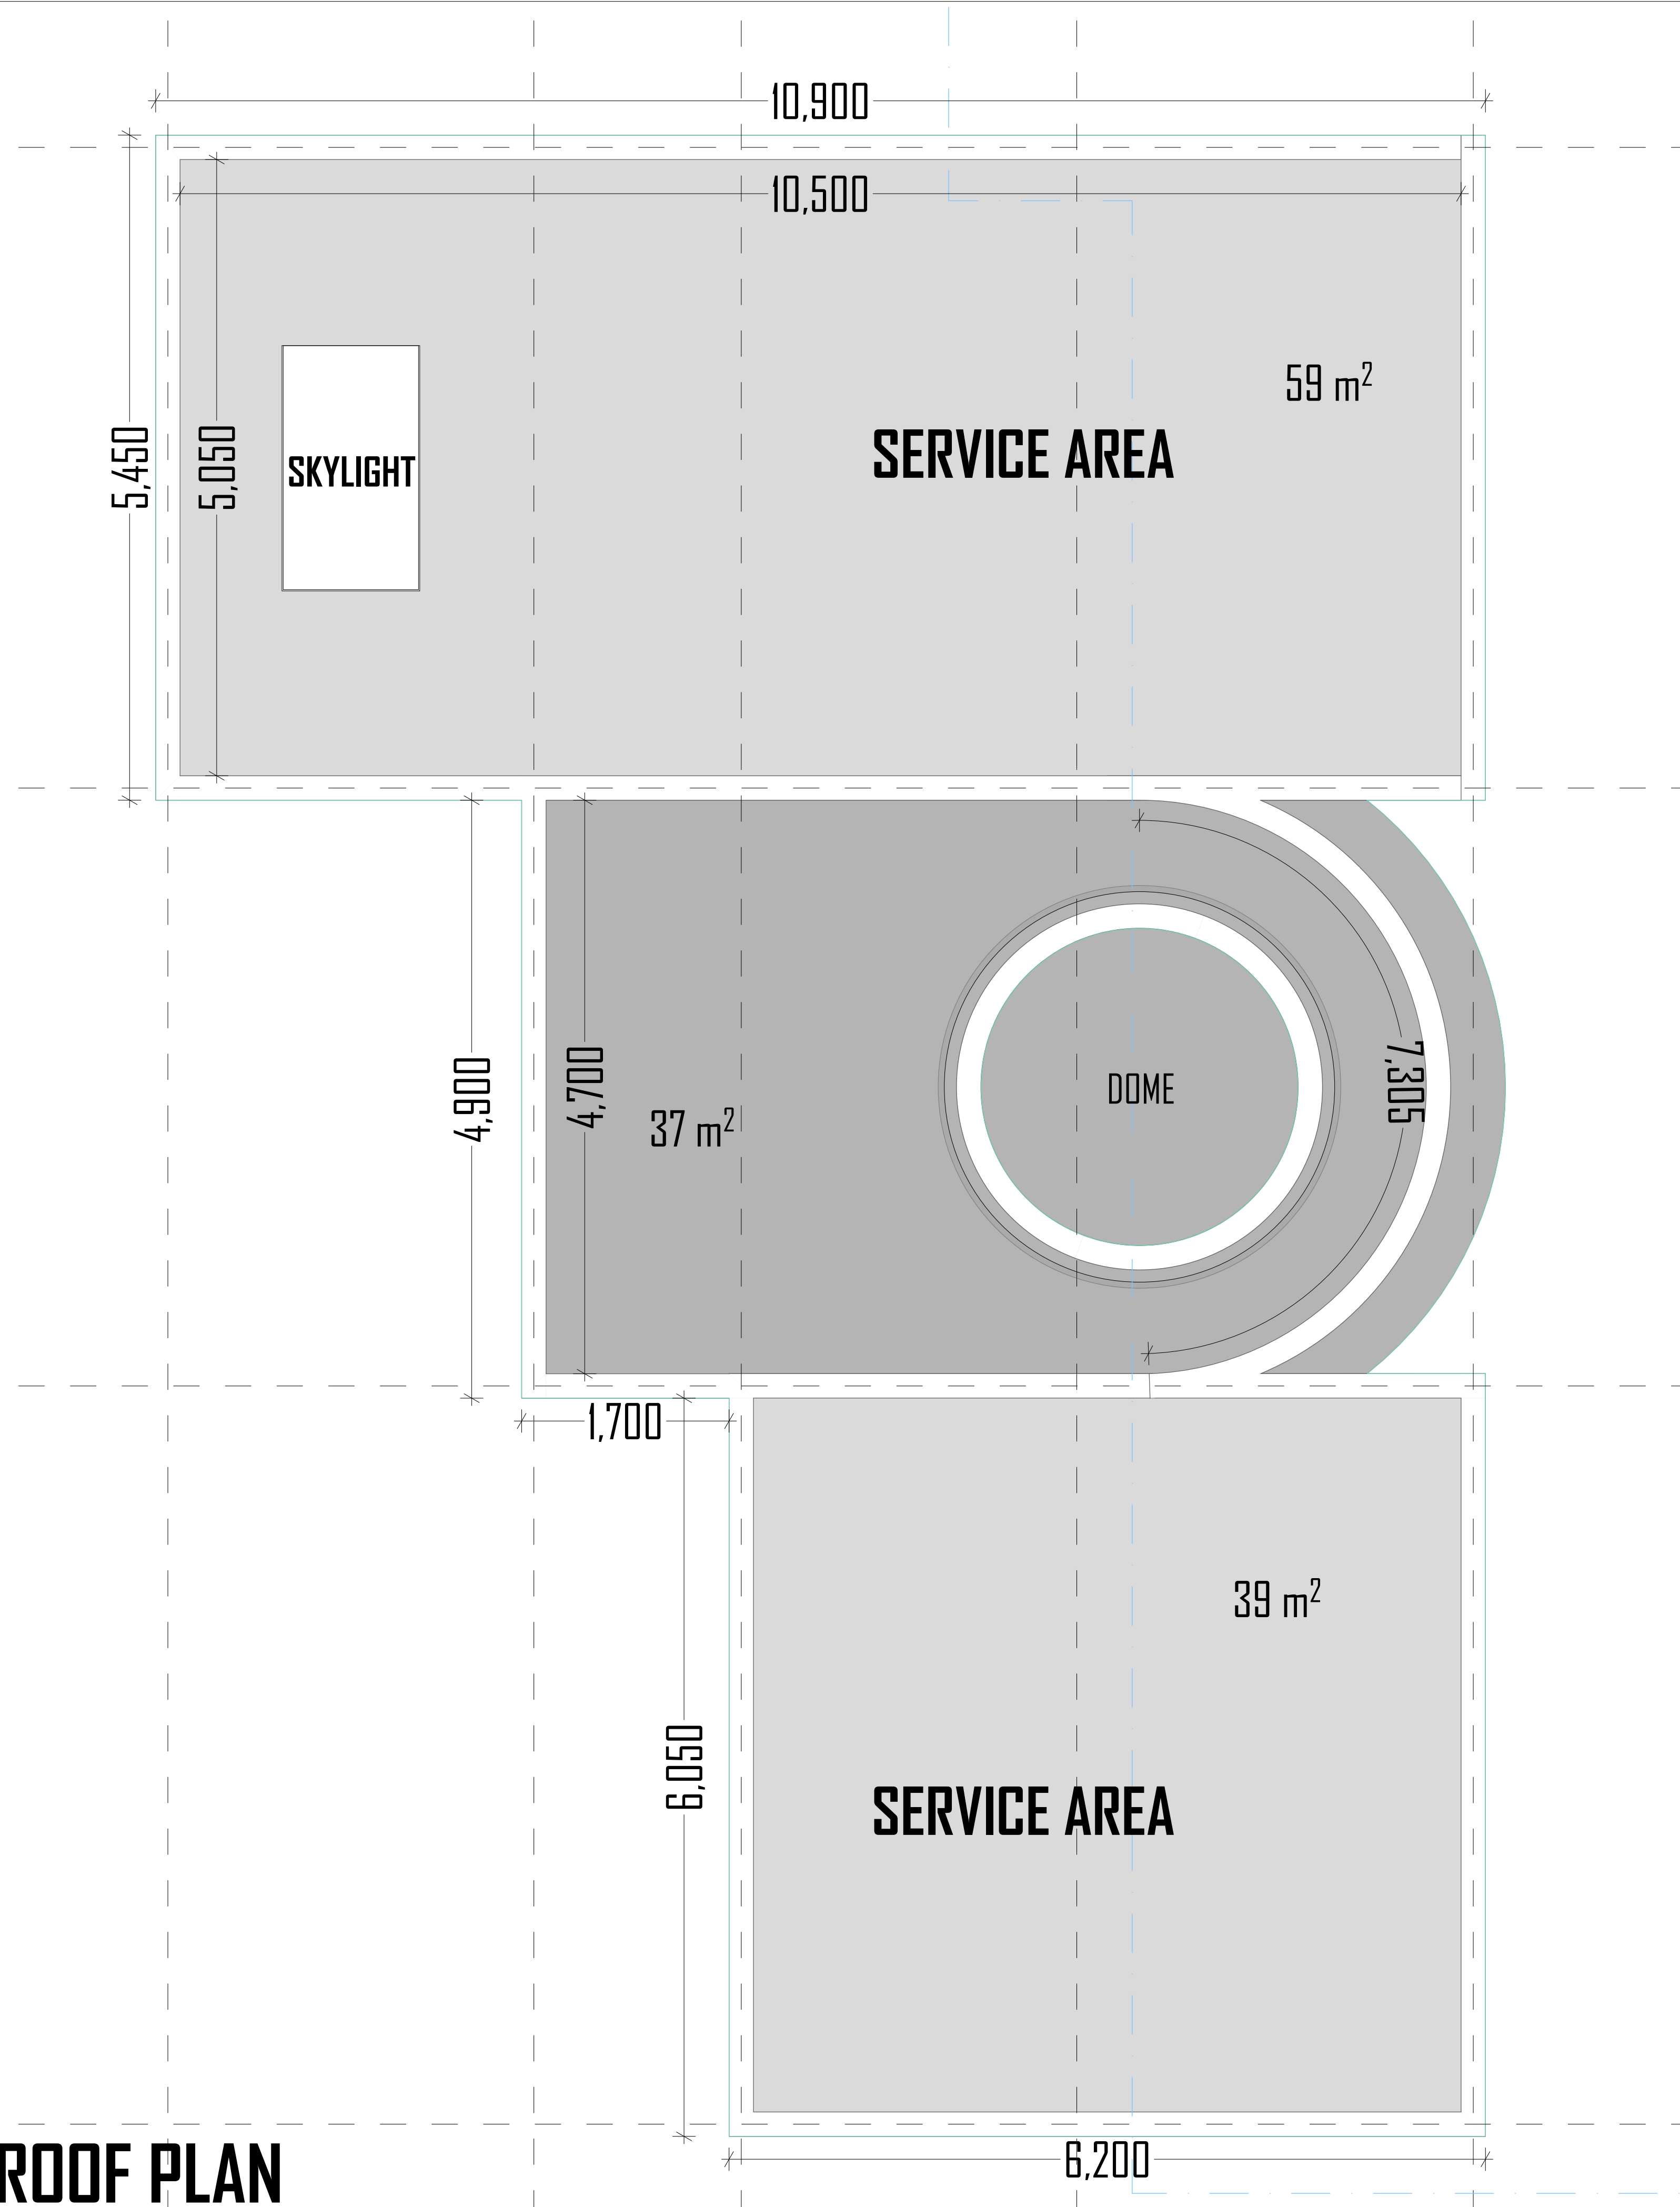

MAIN HOUSE ROOF PLAN

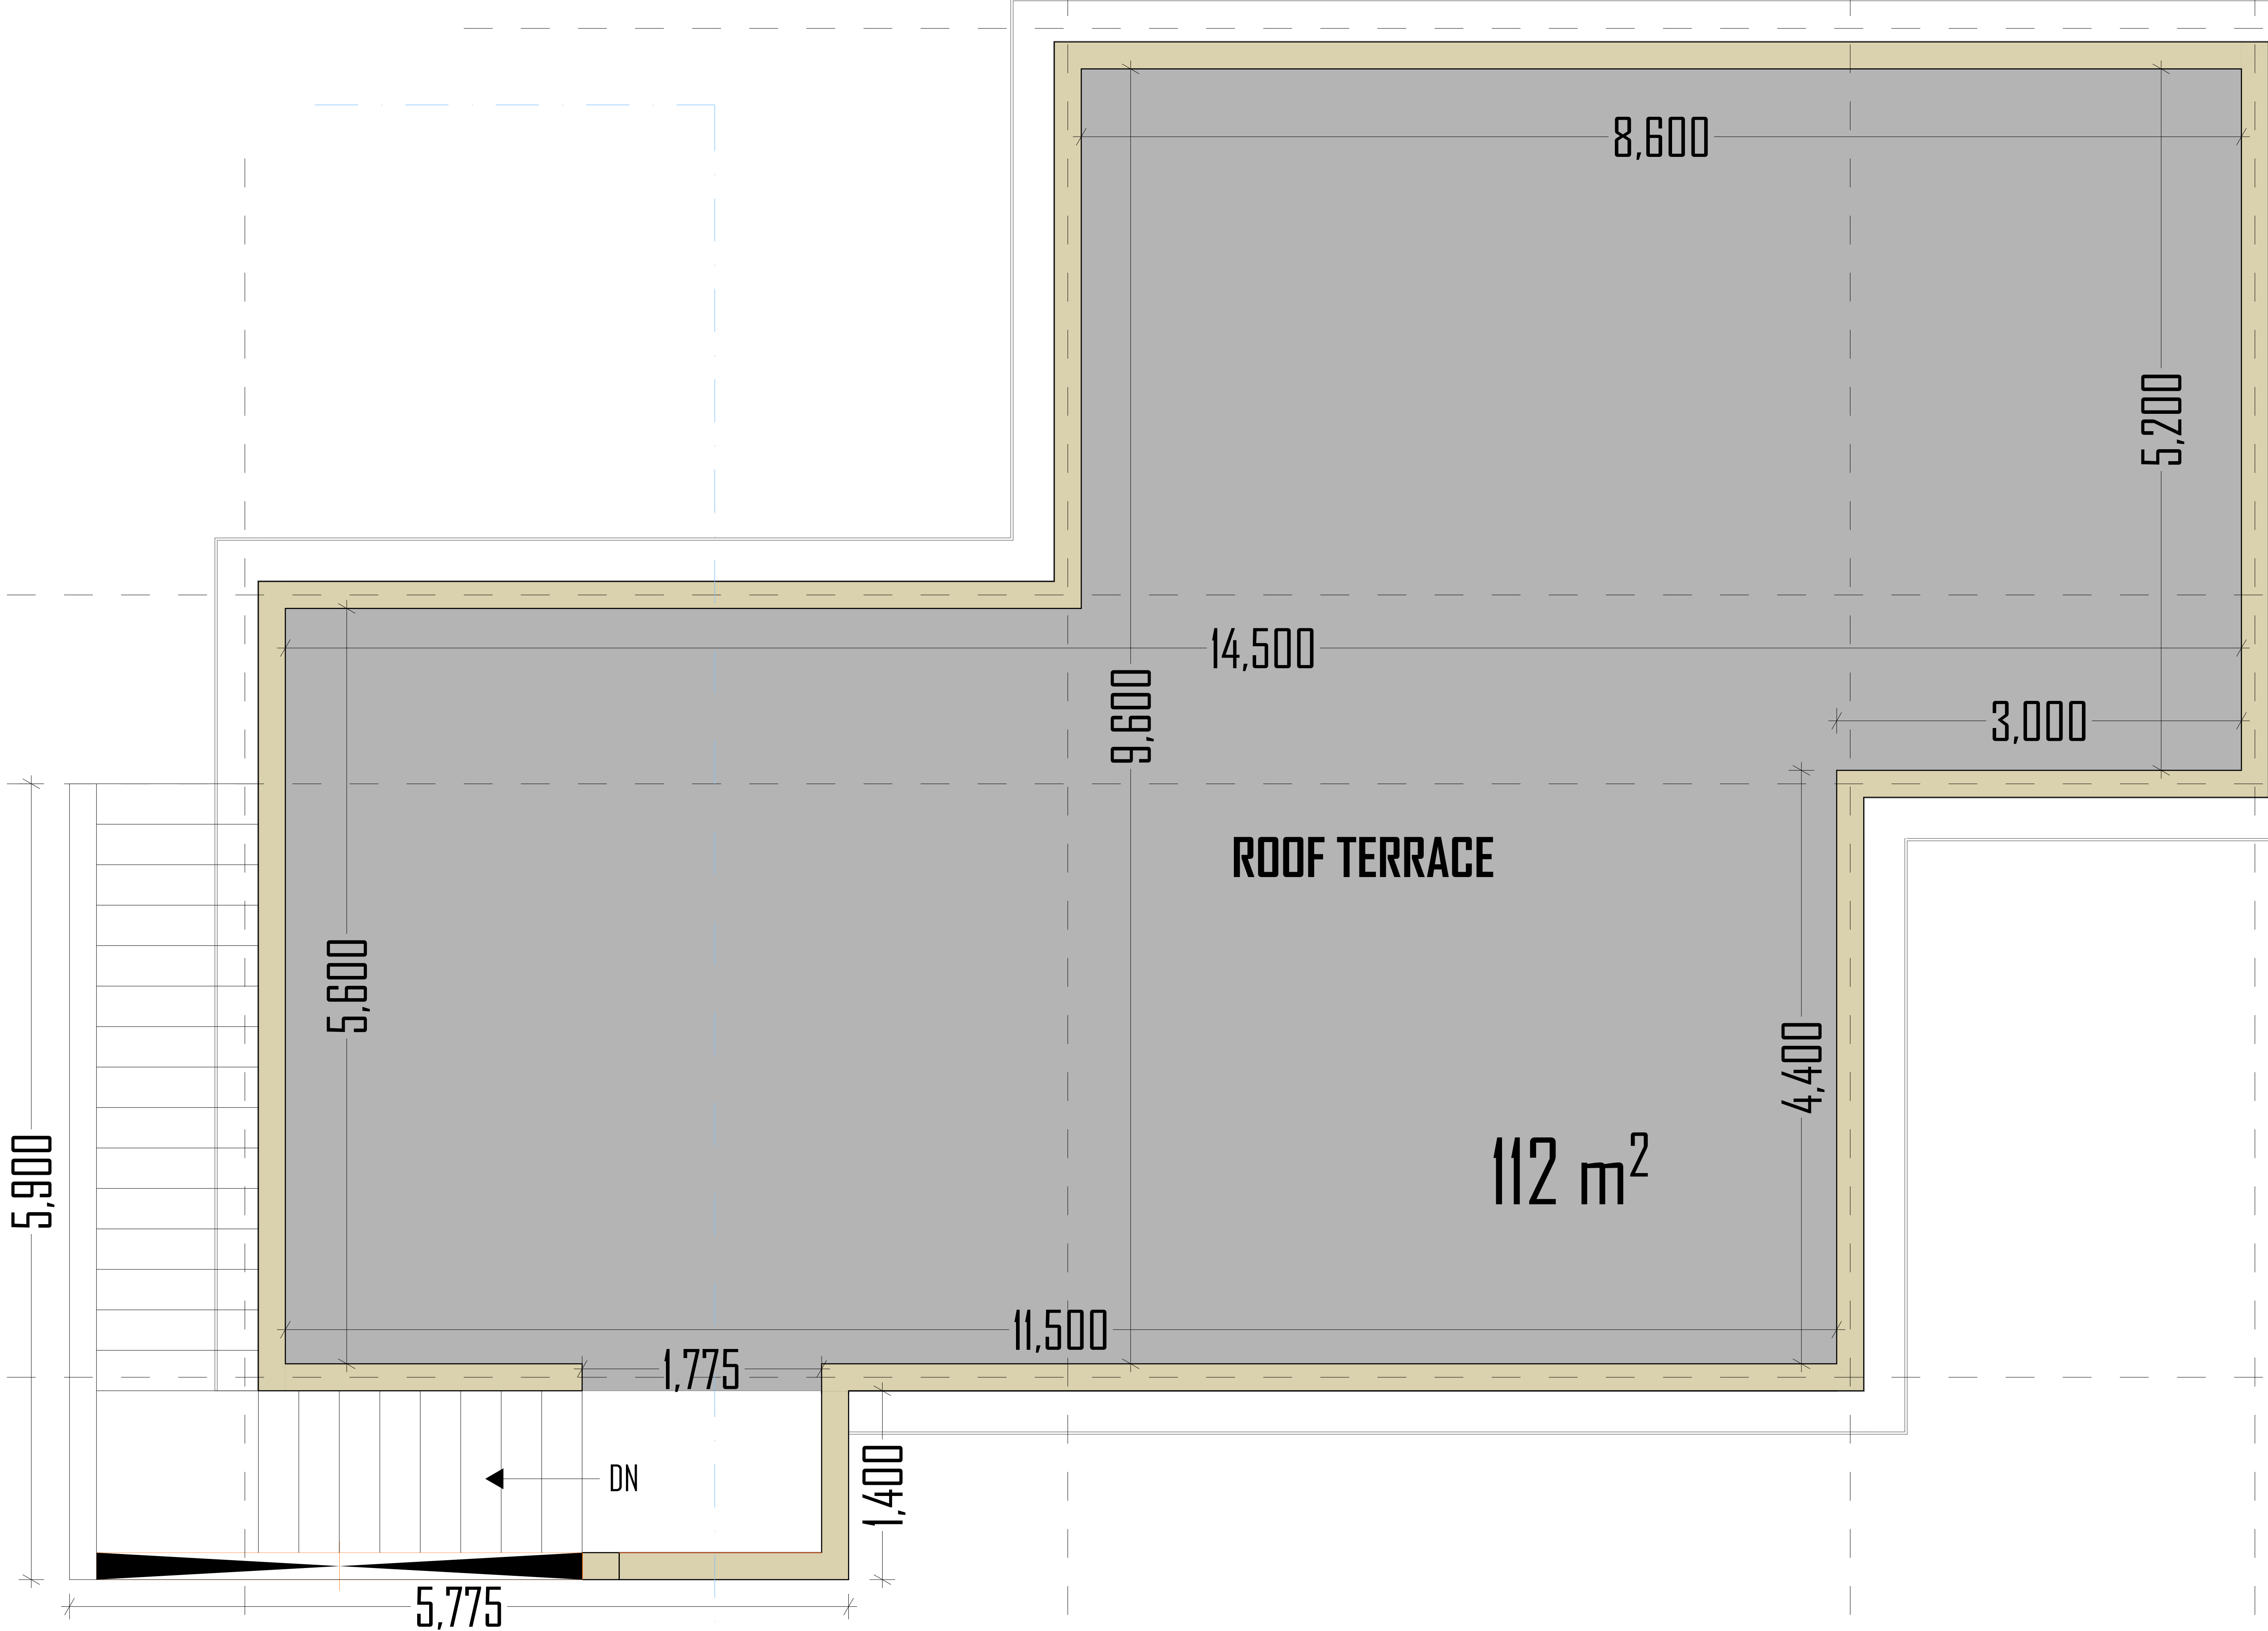

GUEST WING ROOF PLAN

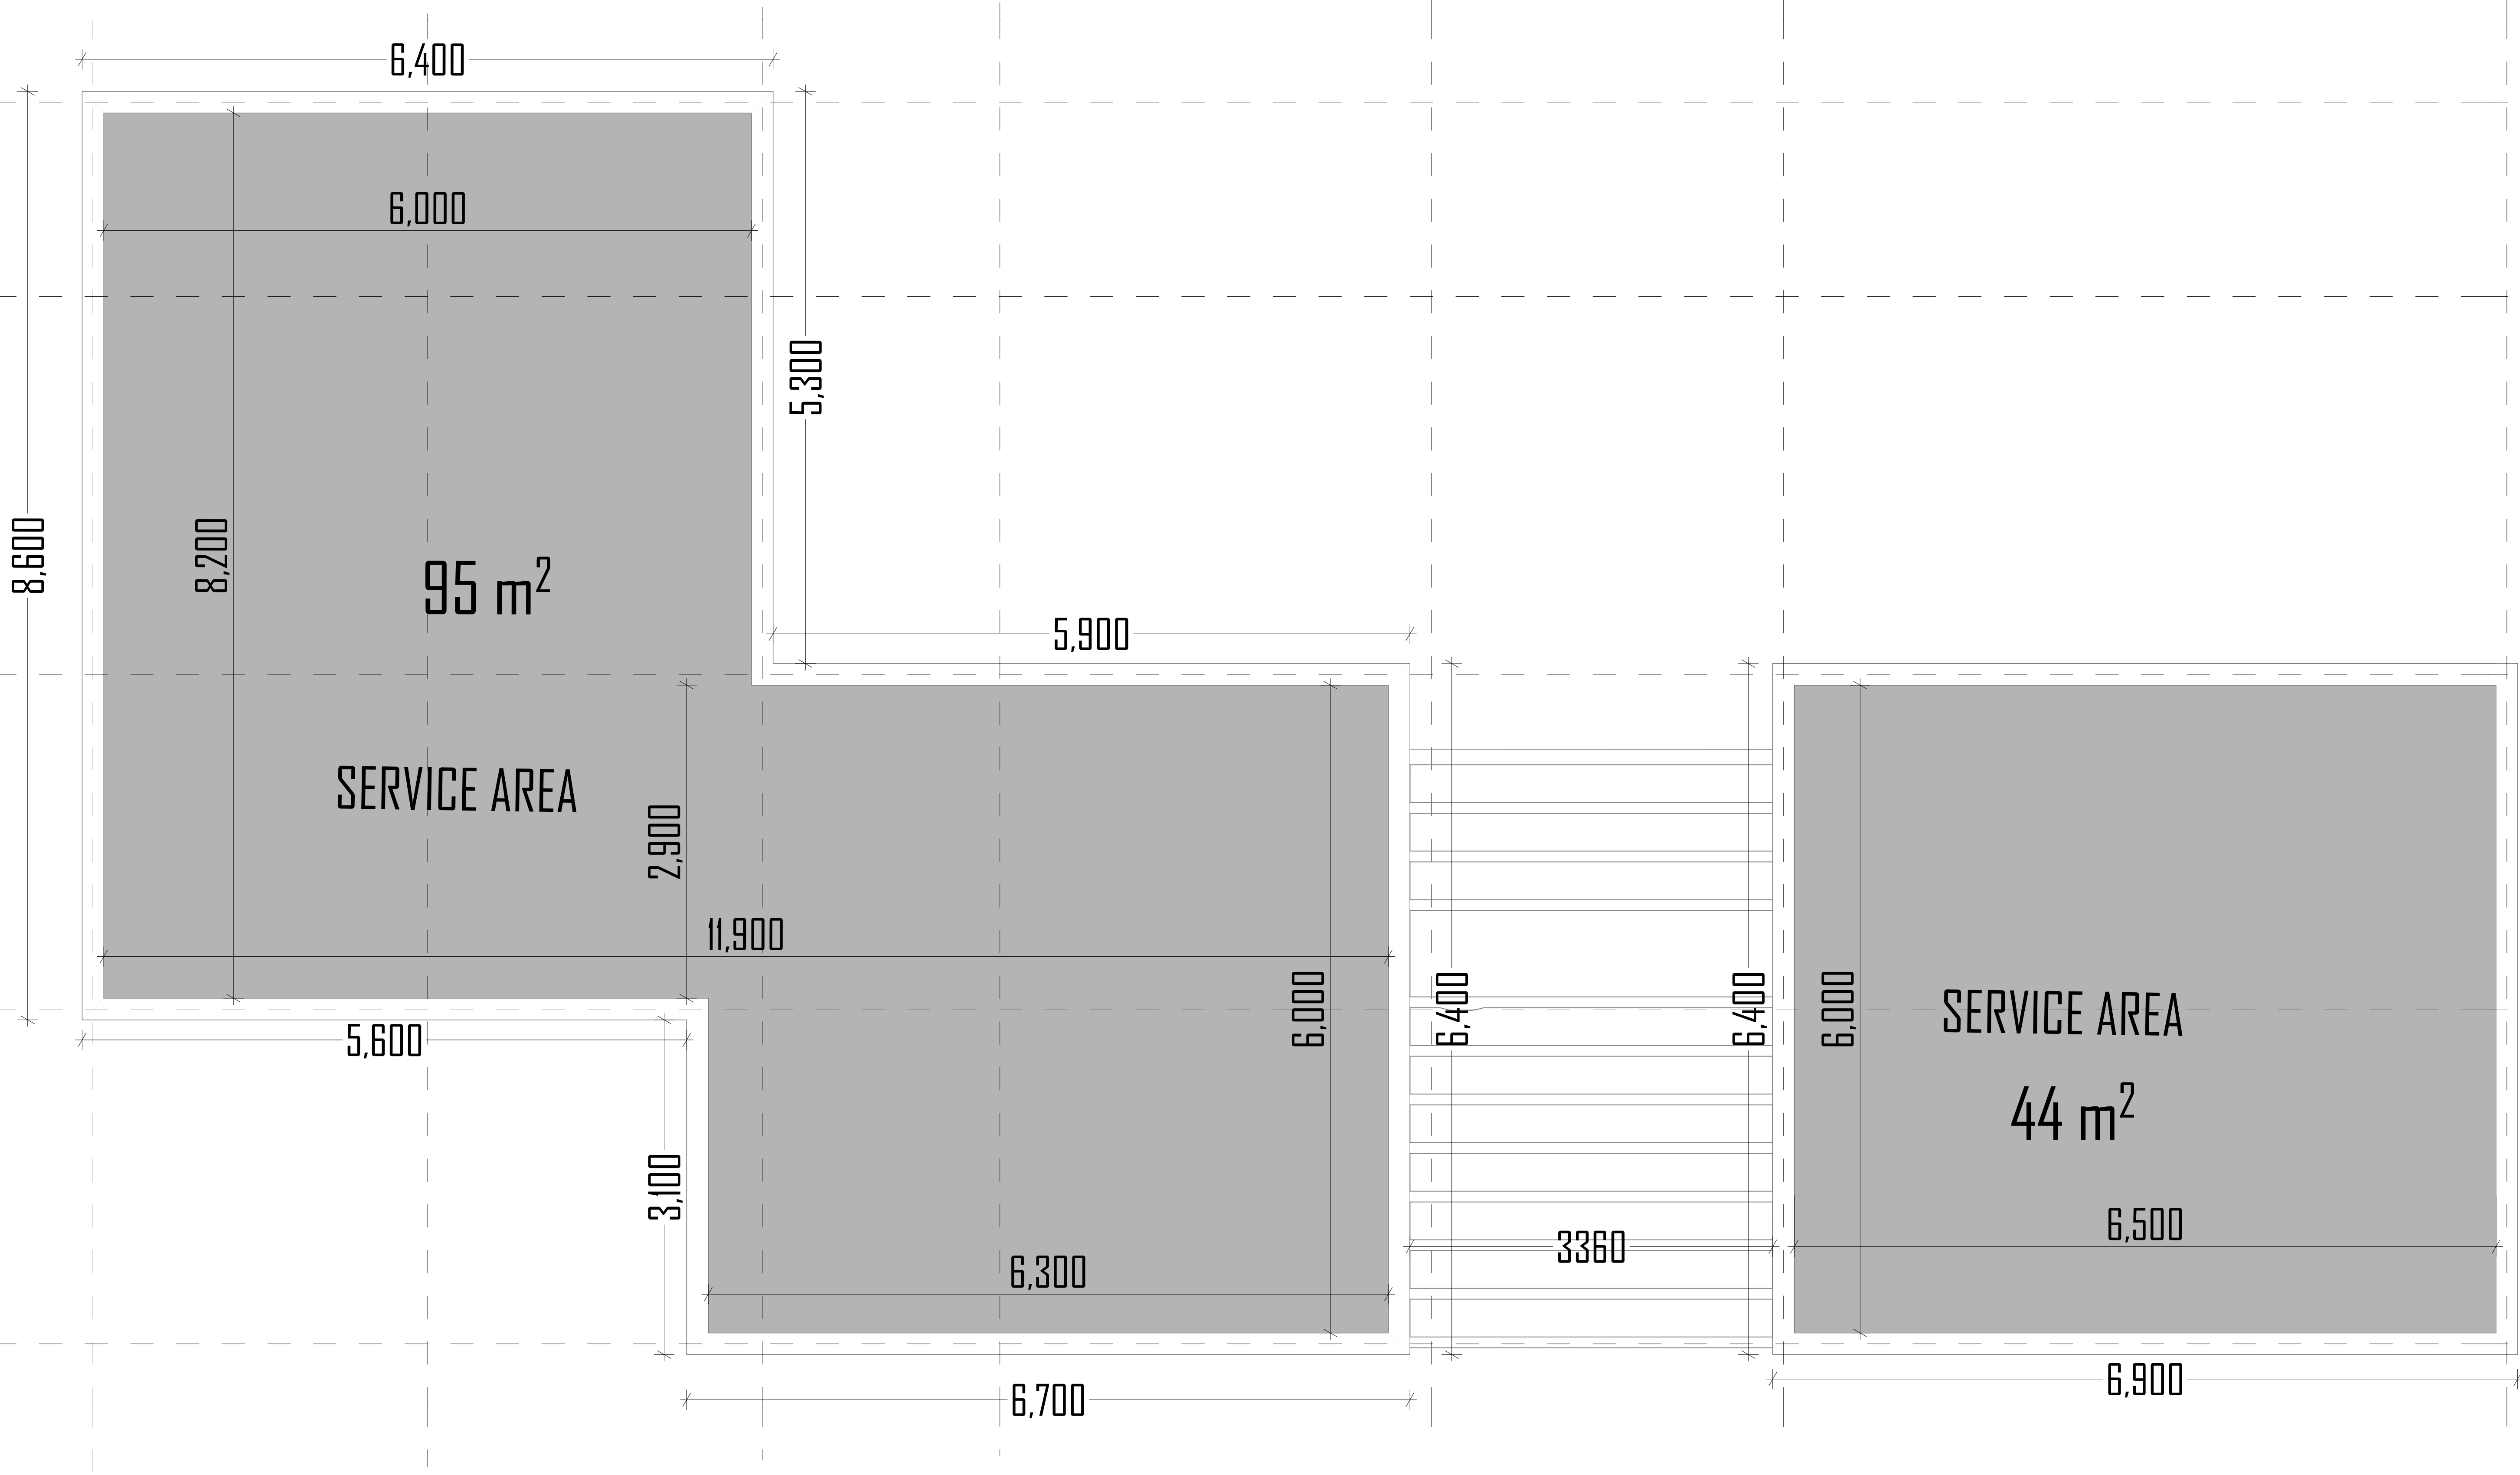

DSQ ROOF PLAN